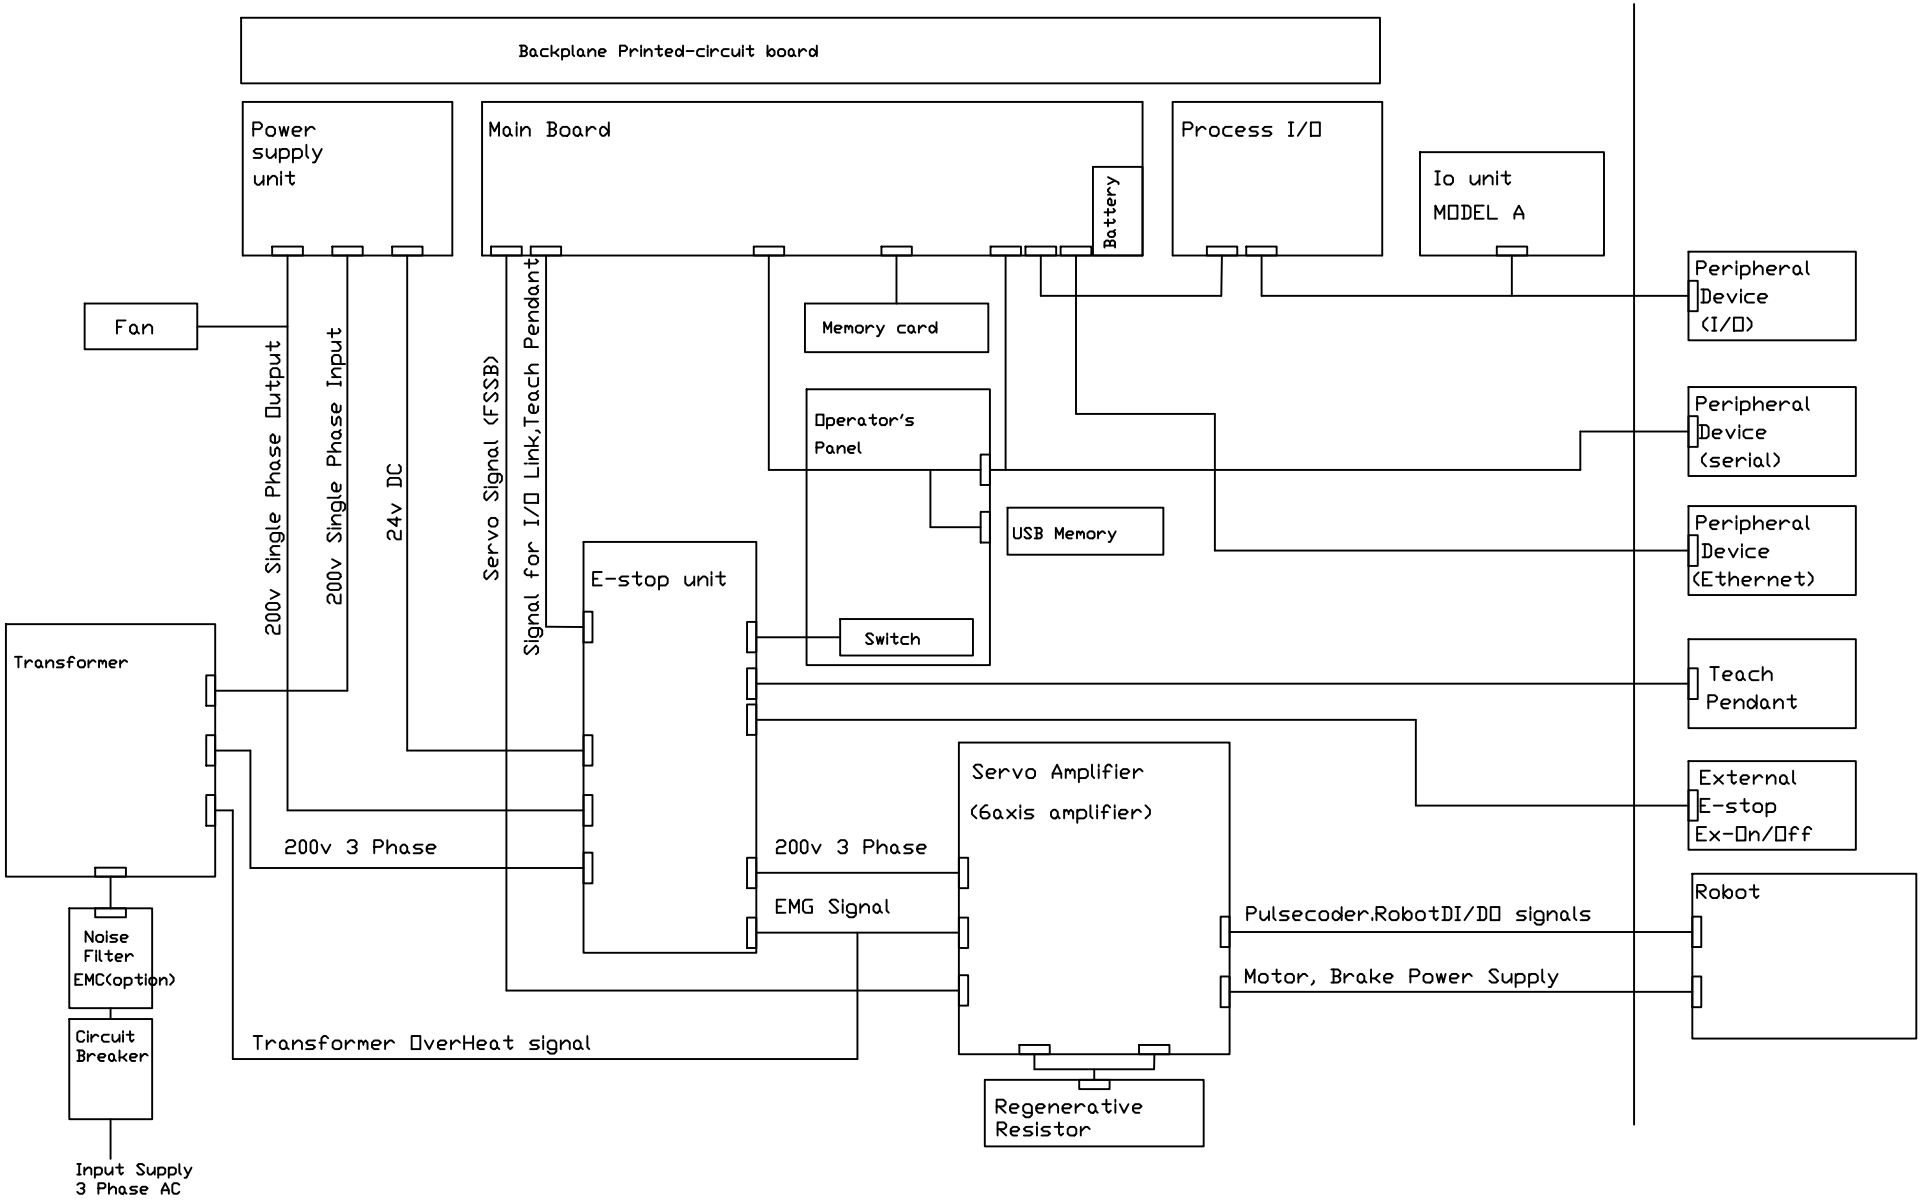

DRAWN		TITLE Robot Block Diagram	ROBOT INTERFACE	TRUMPF METAMATION PVT LTD	DRAWING NO: S-001	=MC
CHECKED						+
APPROVED					CUSTOMER: INTERNAL	Page 3
PROJECT	2025	WORK ORDER : INTERNAL				Next Page 4

36